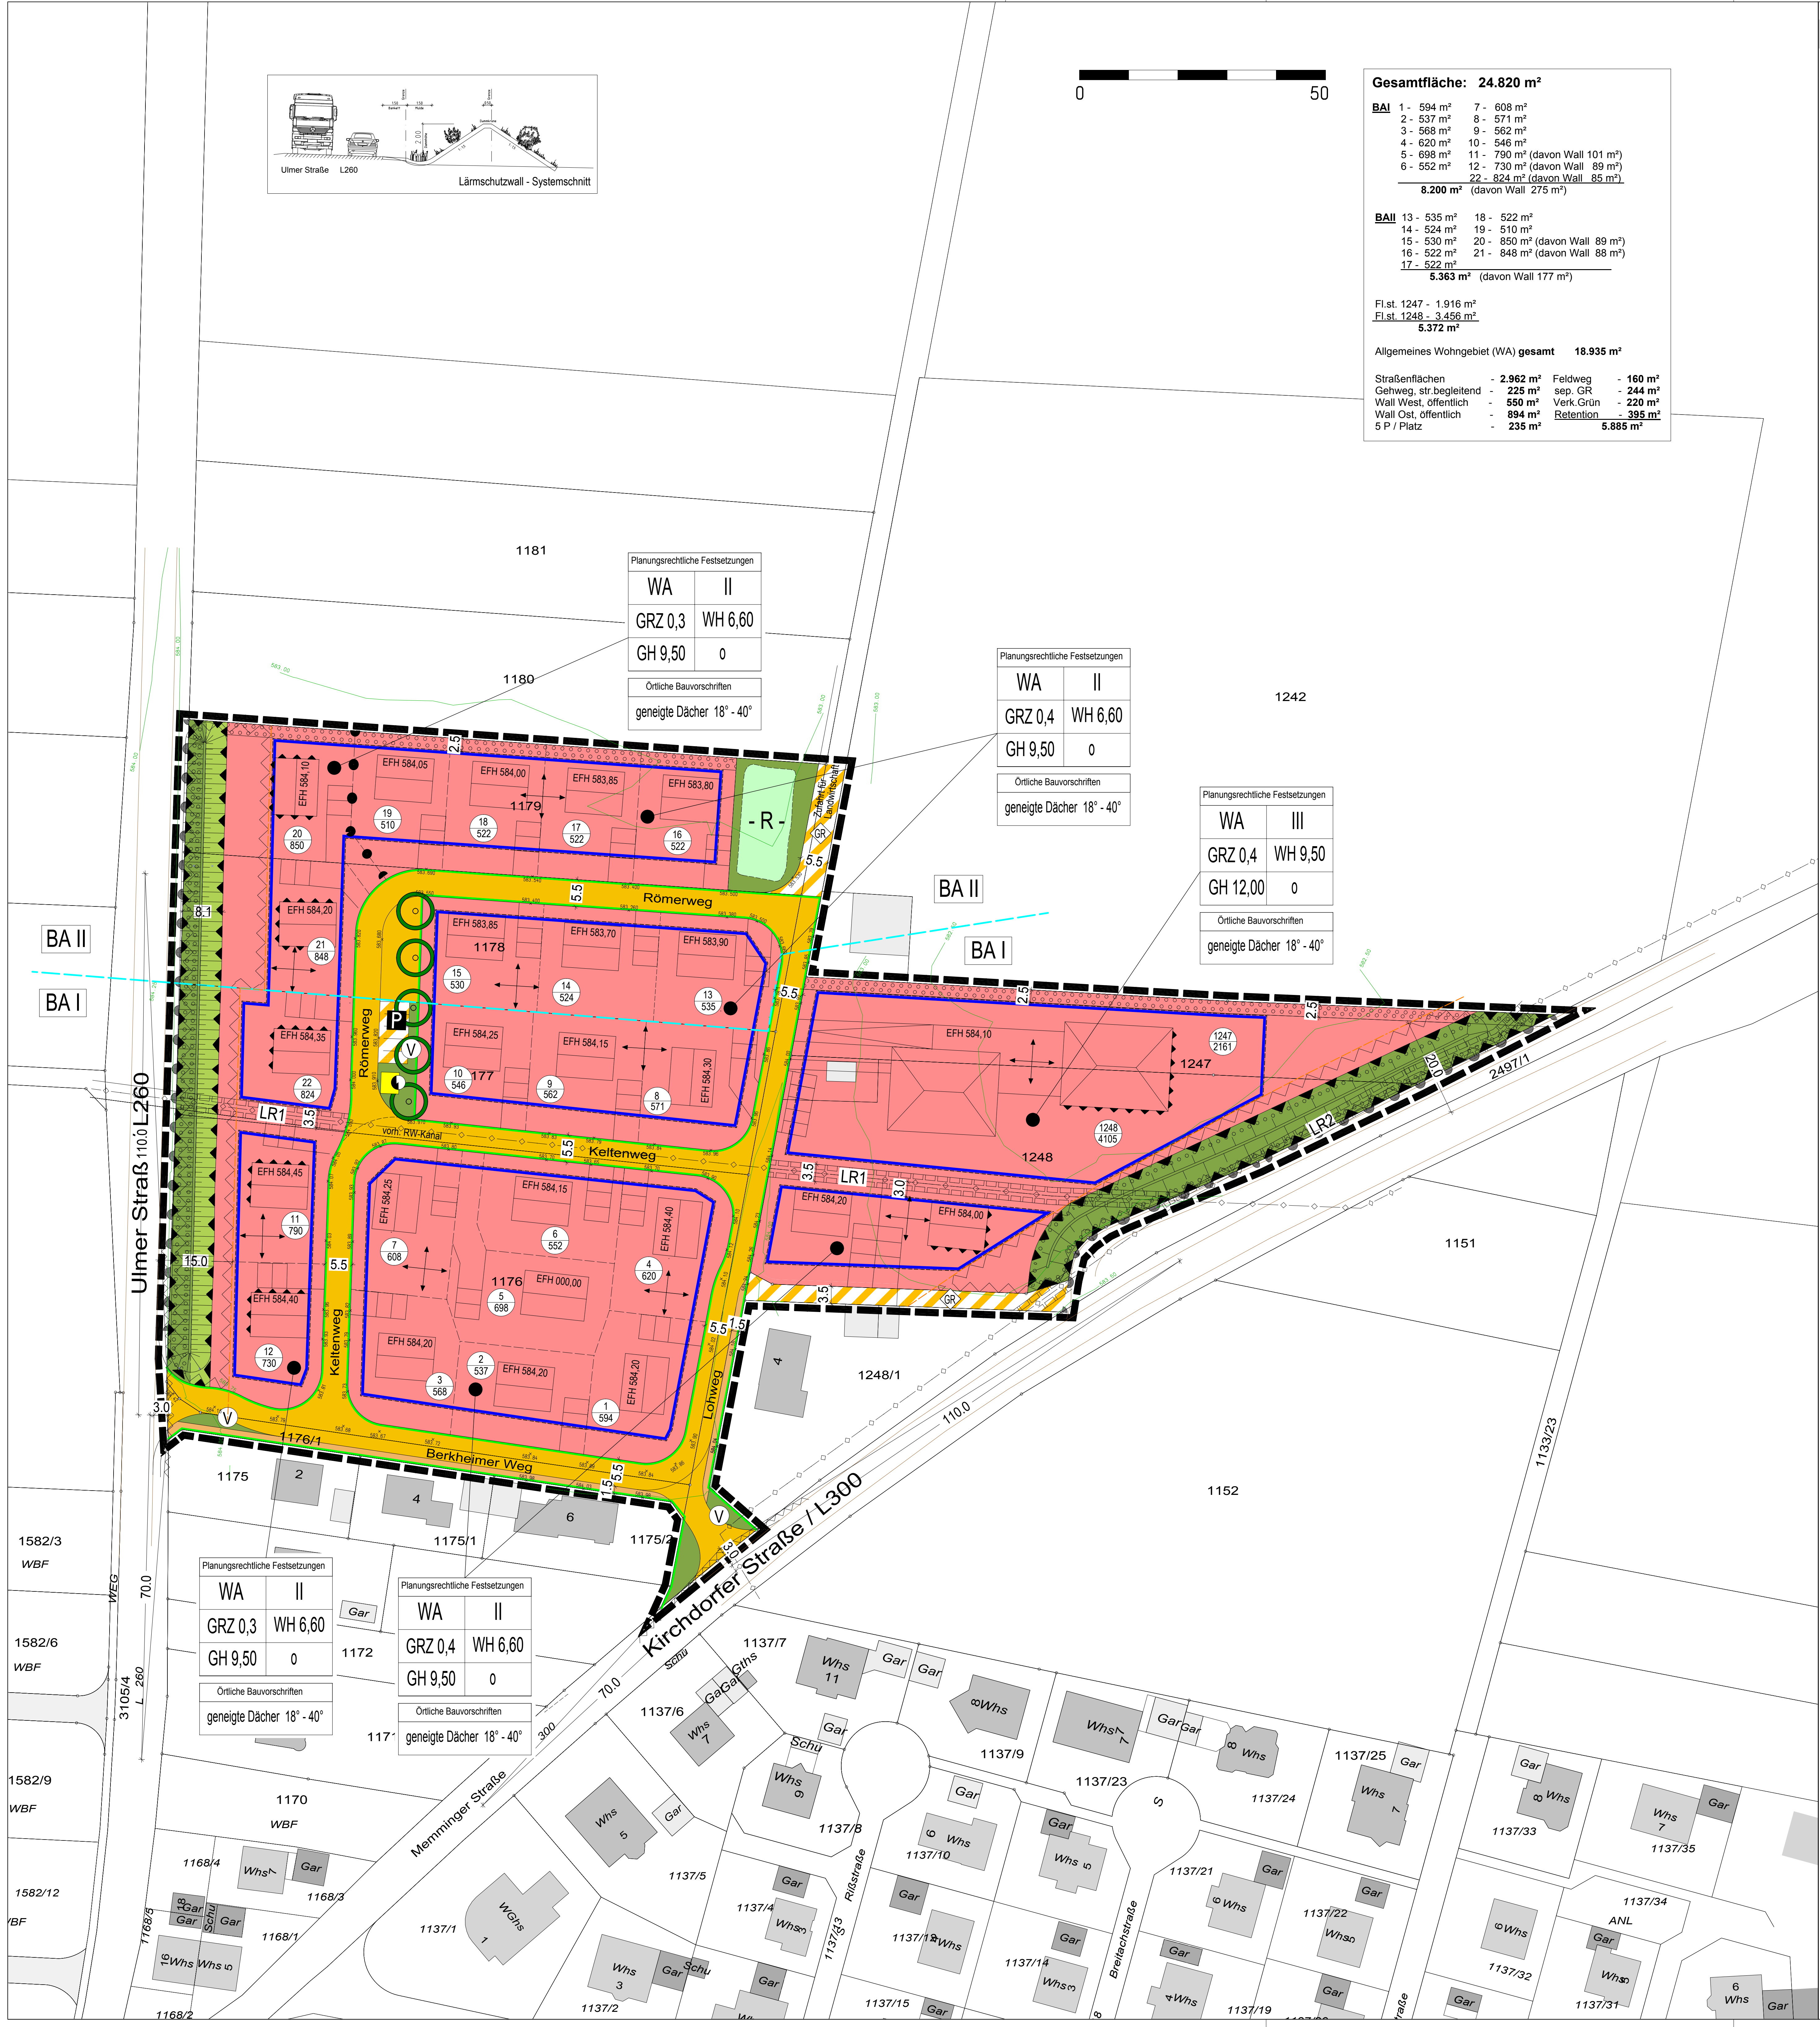

**Gesamtfläche: 24.820 m²**

**BAI**
1 - 594 m²
2 - 537 m²
3 - 568 m²
4 - 620 m²
5 - 698 m²
6 - 552 m²
7 - 608 m²
8 - 571 m²
9 - 562 m²
10 - 546 m²
11 - 790 m² (davon Wall 101 m²)
12 - 730 m² (davon Wall 89 m²)
22 - 824 m² (davon Wall 85 m²)
**8.200 m²** (davon Wall 275 m²)

**BAII**
13 - 535 m²
14 - 524 m²
15 - 530 m²
16 - 522 m²
17 - 522 m²
18 - 522 m²
19 - 510 m²
20 - 850 m² (davon Wall 89 m²)
21 - 848 m² (davon Wall 88 m²)
**5.363 m²** (davon Wall 177 m²)

Fl.st. 1247 - 1.916 m²
Fl.st. 1248 - 3.456 m²
**5.372 m²**

Allgemeines Wohngebiet (WA) **gesamt** **18.935 m²**

| | | | |
|---|---|---|---|
| Straßenflächen | - **2.962 m²** | Feldweg | - **160 m²** |
| Gehweg, str.begleitend | - **225 m²** | sep. GR | - **244 m²** |
| Wall West, öffentlich | - **550 m²** | Verk.Grün | - **220 m²** |
| Wall Ost, öffentlich | - **894 m²** | Retention | - **395 m²** |
| 5 P / Platz | - **235 m²** | | **5.885 m²** |

# TEIL I : TEXTLICHE FESTSETZUNGEN MIT PLANZEICHENERKLÄRUNG

## Rechtsgrundlagen

| | |
|---|---|
| Baugesetzbuch (BauGB) | i.d.F. der Bekanntmachung vom 03. November 2017 (BGBl. I S. 3634) |
| Baunutzungsverordnung (BauNVO) | i.d.F. der Bekanntmachung vom 21. November 2017 (BGBl. I S. 3786) |
| Planzeichenverordnung (PlanzV) | vom 18. Dezember 1990 (BGBl. 1991 I S. 58), zuletzt geändert durch Artikel 3 des Gesetzes vom 04. Mai 2017 (BGBl. I S. 1057) |

Mit Inkrafttreten des Bebauungsplanes treten im Geltungsbereich alle bisherigen Festsetzungen außer Kraft.
In Ergänzung der Planzeichnung wird Folgendes festgesetzt:

## 1. Planungsrechtliche Festsetzungen (§ 9 BauGB und §§ 1-23 BauNVO)

1.1 Art der baulichen Nutzung — § 9 (1) 1 BauGB

W A — 1.1.1 Allgemeines Wohngebiet (WA) — § 4 BauNVO

1.1.1.1 Zulässig im Allgemeinen Wohngebiet sind folgende Nutzungen: — § 4 (2) BauNVO
1. Wohngebäude,
2. die der Versorgung des Gebietes dienenden Läden sowie nicht störende Handwerksbetriebe,
3. Anlagen für kirchliche, kulturelle, soziale, gesundheitliche und sportliche Zwecke.

1.1.1.2 Nicht zulässig im Allgemeinen Wohngebiet sind folgende Nutzungen: — § 1 (5) BauNVO
- Schank- und Speisewirtschaften

1.1.1.3 Die Nutzungen nach § 4 (3) BauNVO: — § 1 (6) 1 BauNVO
1. Betriebe des Beherbergungsgewerbes,
2. sonstige nicht störende Gewerbebetriebe,
3. Anlagen für Verwaltungen,
4. Gartenbaubetriebe,
5. Tankstellen

werden gemäß § 1 (6) 1 BauNVO nicht Bestandteil des Bebauungsplanes und sind daher im Allgemeinen Wohngebiet nicht zulässig.

1.2 Maß der baulichen Nutzung (* Zahlenwerte sind Beispielwerte) — § 9 (1) 1 BauGB

III* — 1.2.1 Höchstzulässige Zahl der Vollgeschosse gem. Planeintrag — § 16 (2) 3 BauNVO, § 20 (1) BauNVO

GRZ 0,4* — 1.2.1 Höchstzulässige Grundflächenzahl gem. Planeintrag — § 16 (2) 1 BauNVO, § 19 (4) BauNVO

Die zulässige Grundfläche darf durch die in § 19 Abs. 4 Satz 1 Nr. 1 + 2 BauNVO bezeichneten Anlagen bis zu 50% überschritten werden, durch die in § 19 Abs. 4 Satz 1 Nr. 3 BauNVO bezeichneten Anlagen (baulichen Anlagen unterhalb der Geländeoberfläche - Tiefgaragen) bis zu einer Grundflächenzahl von max. 0,8.

WH 6,60* — 1.2.2 Höchstzulässige Wandhöhe in m über EFH gem. Planeintrag — § 16 (2) 4 BauNVO, § 18 (1) BauNVO

Oberer Bezugspunkt zur Bemessung der höchstzulässigen Wandhöhe ist der Schnittpunkt der Außenwand bis OK (Oberkante) Dachhaut.

GH 9,50* — 1.2.3 Höchstzulässige Gebäudehöhe in m über EFH gem. Planeintrag — § 16 (2) 4 BauNVO, § 18 (1) BauNVO

Oberer Bezugspunkt zur Bemessung der höchstzulässigen Gebäudehöhe ist beim Satteldach oder geneigtem Dach OK (Oberkante) Firstziegel bzw. Dachhaut.

1.3 Höhenlage der Gebäude (* Zahlenwerte sind Beispielwerte) — § 9 (3) BauGB

EFH 586,60* — 1.3.1 Erdgeschossrohfußbodenhöhe (EFH) in m ü. NN gem. Planeintrasg.

Überschreitungen der EFH sind unzulässig.
Unterschreitungen der EFH sind bis zu 0,20 m zulässig.
Bei Doppelhäusern ist eine gemeinsame EFH auszubilden.

1.4 Bauweise — § 9 (1) 2 BauGB

o — 1.4.1 offene Bauweise — § 22 (2) BauNVO

✥ — 1.4.2 Stellung der baulichen Anlagen - Hauptgebäuderichtung — § 9 (1) 2 BauGB

Die Stellung der baulichen Anlagen wird durch die Hauptgebäuderichtung festgelegt.
Abweichungen von der vorgegebenen Hauptgebäuderichtung bis max. 10° sind zulässig.
Bei sich kreuzenden Symbolen gelten diese alternativ.

1.5 Überbaubare Grundstücksflächen — § 9 (1) 2 BauGB

1.5.1 Baugrenzen — § 23 (1,3) BauNVO

1.5.2 Nicht überbaubare Grundstücksflächen — § 23 (5) BauNVO, i.V.m. §§ 12, 14 BauNVO

In der nicht überbaubaren Grundstücksfläche sind folgende bauliche Anlagen zulässig:
- Zufahrten und Wege,
- Nebenanlagen nach § 14 (1+2) BauNVO (Ausnahmen, siehe Ziffer 2.),
- Tiefgaragen, Garagen, überdachte Stellplätze (Carports) und offene Stellplätze (Einschränkungen siehe Ziffer 2.).

In der nicht überbaubaren Grundstücksfläche sind innerhalb der Anbauverbotsstreifen entlang der Landesstraßen Hochbauten, bauliche Anlagen und Nebenanlagen, welche nach § 14 BauNVO in einem Baugebiet auch außerhalb der Baugrenzen zulässig sein können, nicht zulässig.
In den nicht überbaubaren Grundstücksflächen sind öffentliche Versorgungsanlagen für die Straßenbeleuchtung zu dulden.

1.6 Flächen für Garagen, überdachte Stellplätze (Carports) und offene Stellplätze — § 9 (1) 4 BauGB

Tiefgaragen, Garagen, überdachte Stellplätze (Carports) und offene Stellplätze sind innerhalb und außerhalb der überbaubaren Grundstücksfläche zulässig.
Garagen sind zwingend mit mindestens 5,00 m Abstand zur öffentlichen Verkehrsfläche zu errichten, bei Parallelstellung zur öffentlichen Verkehrsfläche und bei ferngesteuerten Toranlagen ist ein Mindestabstand von 1,0 m einzuhalten. Carports sind mit mindestens 1,0 m Abstand zur öffentlichen Verkehrsfläche zu errichten.

1.7 Von der Bebauung freizuhaltende Flächen — § 9 (1) 10 BauGB

Die im Lageplan ausgewiesenen Sichtflächen sind von baulichen Anlagen und von Sichtbehinderungen zwischen 0,80 m und 2,00 m Höhe über Fahrbahnoberkante freizuhalten.

Zur Bepflanzung zulässig sind:
- Großkronige Bäume mit Kronenansatz über 2,0 m Höhe.

1.8 öffentliche Verkehrsflächen — § 9 (1) 11 BauGB

1.8.1 Straßenbegrenzungslinie — § 9 (1) 11 BauGB
Verkehrsfläche
Gehweg
Straßenbegrenzungslinie

1.8.2 Verkehrsflächen besonderer Zweckbestimmung — § 9 (1) 11 BauGB

P — 1.8.2.1 Zweckbestimmung: öffentliche Parkierung

GR — 1.8.2.2 Zweckbestimmung: öffentlicher Geh- und Radweg

V — 1.8.3 Verkehrsgrün als Bestandteil der Verkehrsfläche — § 9 (1) 11 BauGB

In den gekennzeichneten Flächen ist die Errichtung von Nebenanlagen nach § 14 (1) BauNVO grundsätzlich unzulässig.

1.8.4 Bereich ohne Ein- und Ausfahrt — § 9 (1) 11 BauGB

1.9 Fläche für Versorgungsanlagen — § 9 (1) 12 BauGB
hier: Umspannstationen

1.10 Versorgungsleitungen — § 9 (1) 13 BauGB
hier: vorhandener Regenwasserkanal / vorhandene Wasserleitung

1.11 Führung von Versorgungsanlagen und -leitungen — § 9 (1) 13 BauGB

Sämtliche Ver- und Entsorgungsleitungen sind mit Ausnahme erforderlicher Umspannstationen unterirdisch zu führen.

1.12 Flächen für die Rückhaltung und Versickerung von Niederschlagswasser — § 9 (1) 14 BauGB

- R - — Die im Plan festgesetzte Fläche für die Regenwasserrückhaltung **- R -** ist als offene Mulde auszubauen. Fremd-, Tag- und Quellwasser darf nicht der Gesamtwasserkanalisation zugeleitet werden. Das Oberflächenwasser der Verkehrsflächen ist dem geplanten Regenwasserrückhaltebereich zuzuführen.

1.13 Grünflächen — § 9 (1) 15 BauGB

1.13.1 öffentliche Grünflächen
hier: Lärmschutzwall / Fläche für Retention

1.13.1 private Grünflächen
hier: Lärmschutzwall

1.14 Planungen, Nutzungsregelungen, Maßnahmen und Flächen für Maßnahmen zum Schutz, zur Pflege und zur Entwicklung von Boden, Natur und Landschaft / — § 9 (1) 20,25 BauGB, § 9 (1) 15 BauGB

1.14.1 Maßnahmen zur Eingriffsverringerung, -minimierung — § 9 (1) 20 BauGB

1.14.1.1 Umgrenzung von Flächen zum Anpflanzen von Bäumen, Sträuchern und sonstigen Bepflanzungen — § 9 (1) 25a BauGB

• straßenseitige Begrünung der 2 Lärmschutzwälle gem. Pflanzliste 1:
Einsaat der Fläche (RSM 8.1: Biotopflächen, artenreiches Extensiv-Grünland) mit extensiver Bewirtschaftung.
Pflanzung von standortgerechten, heimischen Laubgehölzen (in gruppenweiser Anordnung, stufig und artenreich angelegt).
• Ortsrandeingrünung an der nördlichen Plangebietsgrenze gem. Pflanzliste 1:
Pflanzung von standortgerechten, heimischen Laubgehölzen (in gruppenweiser Anordnung, stufig und artenreich angelegt). In diesem Übergangsbereich zur freien Landschaft sind Nadelgehölze unzulässig.

1.14.1.2 Pflanzgebot von Bäumen und Sträuchern — § 9 (1) 25a BauGB

An den im Lageplan zeichnerisch festgesetzten Standorten sind standortgerechte Bäume oder Pflanzungen gem. Pflanzenliste zu pflanzen, zu pflegen, dauerhaft zu erhalten und bei Abgang zu ersetzen. Der gekennzeichnete Standort kann der gegebenen Situation angepasst werden.
Der Abstand von Ver- und Entsorgungsleitungen zum Stamm soll mindestens 2,50 m betragen. Bei geringeren Abständen sind Vorkehrungen (Rohrummantelung, humusfreier Mineralboden etc.) zum Schutz vor Baumwurzeln erforderlich.

1.14.1.3 Sonstige Minimierungsmaßnahmen — § 9 (1) 20 BauGB

- Private Grünflächen sind weitgehend naturnah mit standortgerechten Pflanzen und artenreichen Wiesenmischungen zu gestalten und zu pflegen. (vgl. Pflanzliste Nr. 1 + 4).
- Es wird empfohlen, flach geneigte Dachflächen (z.B. von Garagen) extensiv zu begrünen.
- Zudem ist eine Insektenfreundliche Beleuchtung zu verwenden (Natriumdampflampen oder LED-Leuchten).

1.14.2 Maßnahmen zum Artenschutz — § 9 (1) 20 BauGB

- Anbringung von 3 Nistkästen an geeigneten Stellen nach Ende der Brutperiode

1.14.3 Pflanzliste 1

Freiwachsende, heckenartige Gehölzstrukturen für öffentliche und private Grünflächen mit Biotopverbundfunktion entlang von Grundstücksgrenzen; empfohlene Pflanzgröße: verpflanzt 100-150

| | | | |
|---|---|---|---|
| Acer campestre | Feld-Ahorn | Prunus spinosa | Schlehe |
| Carpinus betulus | Hainbuche | Rosa canina | Hundsrose |
| Corylus avellana | Haselnussstrauch | Pyrus communis | Wildbirne |
| Cornus sanguinea | Roter Hartriegel | Sambucus nigra | Schwarzer Holunder |
| Euonymus europaeus | Pfaffenhütchen | Viburnum lantana | Wolliger Schneeball |
| Ligustrum vulgare | Gewöhnlicher Liguster | Viburnum opulus | Gemeiner Schneeball |
| Prunus avium | Gemeine Kirsche | | |

Pflanzliste 2

Straßenbaum, empfohlene Pflanzgröße:
Hochstamm 3xv 12-14

| | |
|---|---|
| Acer pseudoplatanus | Bergahorn |
| Quercus robur | Stieleiche |
| Tilia cordata | Winter-Linde |

Pflanzliste 3

Fassadenbegrünung

| | |
|---|---|
| Clematis in Sorten | Waldrebe |
| Hedera hibernica | Irländischer Efeu |
| Hydrangea petiolaris | Kletterhortensie |
| Lonicera in Sorten | Geißblatt |
| Parthenocissus quinquefolia | Wilder Wein |
| Rosa spec. o.ä. | Kletterrose |

Pflanzliste 4

Regionaltypische Obsthochstämme für private Grünflächen; empfohlene Pflanzgröße: Hochstamm 8/10

| | | |
|---|---|---|
| Äpfel | Birnen | Zwetschgen |
| Bohnapfel | Bartholomäusbirne | Hauszwetschge |
| Glockenapfel | Fasslesbirne | Lukas Frühzwetschge |
| Goldparmäne | Junkersbirne | Schöne aus Löwen |
| Jakob Fischer | Schweizer Wasserbirne | Bühler Zwetschge |
| Maunzenapfel | Palmischbirne | o.ä. |
| Schwäbischer | o.ä. | |

Saatmischung für öffentliche Grünfläche:
z.B. von Rieger-Hofmann GmbH (In den Wildblumen 7, 74572 Raboldshausen) oder von Saaten Zeller (Erftalstr. 6, 63928 Riedern) RSM 8.1 Biotopflächen, artenreiches Extensivgrünland Variante 1 - Ansaatstärke: (3-7 g /m²) / Empfohlen werden 1-2 Schnitte im Jahr.
*(Findet Verwendung für Ausgleichs- und Biotopentwicklungsflächen an Verkehrswegen, extensiv genutzten und gepflegten Flächen im öffentlichen Grün.)*

1.15 Mit Geh-, Fahr- oder Leitungsrechten (GR - FR - LR) zu belastende Flächen — § 9 (1) 21 BauGB

LR1 - Leitungsrecht (LR) Regenwasserkanal zugunsten der Gemeinde
LR2 - Leitungsrecht (LR) Wasserleitung zugunsten der Gemeinde
Die mit Leitungsrechten versehenen Flächen dürfen nicht überbaut oder durch Pflanzungen beeinträchtigt werden.
Ausnahme: Die vorhandene Wasserleitung darf entlang der L300 durch einen Lärmschutzwall überbaut werden.

1.16 Technische Vorkehrungen zum Schutz vor schädlichen Umwelteinwirkungen — § 9 (1) 24 BauGB

Aktive Lärmschutzmaßnahme:
Entlang der L 260 und entlang der L 300 sind an den in der Planzeichnung eingetragenen Stellen Lärmschutzwälle mit einer Höhe von 2 m über Gelände zu erstellen.

Passive Lärmschutzmaßnahmen:
An den Westfassaden von Gebäuden auf den Grundstücken 20 und 21 sind öffenbare Fenster von Aufenthaltsräumen unzulässig. Dies gilt nicht für Aufenthaltsräume im EG.

An den in der Planzeichnung gekennzeichneten Fassaden sind bei Schlafräumen und bei Räumen mit sauerstoffverbrauchender Energiequelle schallgedämmte Lüftungseinrichtungen erforderlich.
Die Schalldämmung der Außenbauteile ist nach DIN 4109-1:2018-01 "Schallschutz im Hochbau - Teil 1: Mindestanforderungen" und DIN 4109-2:2018-01 "Schallschutz im Hochbau - Teil 2: Rechnerische Nachweise" zu bemessen. Der Nachweis ist im Baugenehmigungsverfahren zu erbringen.
Die dabei zugrunde zu legenden erforderlichen Schalldämmmaße können der Anlage 5 der schalltechnischen Untersuchung ACB-0318-8151/04 der ACCON GmbH vom 23.03.2018 entnommen werden. Alternativ kann die Lärmsituation eines konkreten Bauvorhabens gezielt berechnet und das erforderliche Schalldämmmaß dadurch ermittelt werden. In diesem Fall ist ein entsprechendes schalltechnisches Gutachten unaufgefordert mit dem Bauantrag vorzulegen.

1.17 Sonstige Festsetzungen durch Planzeichen

1.17.1 Planbereich — § 9 (7) BauGB
Grenze des räumlichen Geltungsbereichs des Bebauungsplanes

1.17.2 Abgrenzung unterschiedlicher Art und Maß der baulichen Nutzung — § 16 (5) BauNVO

1.16.3 Nutzungsschablone

| Planungsrechtliche Festsetzungen | |
|---|---|
| 1 | 2 |
| 3 | 4 |
| 5 | 6 |

Füllschema der Nutzungsschablone
1 - Art der baulichen Nutzung
2 - höchstzulässige Zahl der Vollgeschosse
3 - höchstzulässige Grundflächenzahl (GRZ)
4 - höchstzulässige Wandhöhe (WH) in m über EFH
5 - höchstzulässige Gebäudehöhe (GH) in m über EFH
6 - Bauweise

## 2. Nachrichtliche Übernahme § 9 (6) BauGB

**15,0 m / 20 m Abstandsfläche von baulichen Anlagen zur Landesstraße L260 - Anbauverbotsstreifen**
**20 m Abstandsfläche von baulichen Anlagen zur Landesstraße L300 - Anbauverbotsstreifen**

Nebenanlagen, welche nach § 14 BauNVO in einem Baugebiet auch außerhalb der Baugrenzen zulässig sein können, dürfen innerhalb des vorgenannten Anbauverbots nicht ohne die ausdrückliche der Straßenbauverwaltung zugelassen werden.
Nach der LBO genehmigungsfreie Anlagen bedürfen in diesem Bereich der Befreiung vom Anbauverbotsstreifen durch die Straßenbauverwaltung.

## 3. Hinweise

3.1 Sonstige Planzeichen (keine Festsetzung)

vorhandene Grundstücksgrenzen
geplante Grundstücksgrenzen

1176 — Flurstücknummern

vorhandene Wohn- u. Nebengebäude

geplante Gebäude / Gebäudevorschlag (beispielhaft)

5.00 — Maßlinie (beispielhaft)

3/650 — Kennziffer und Fläche in m² geplanter Grundstücke

3.2 Unterirdische Leitungen
Vor jeglichen Bauarbeiten ist bei den Versorgungsträgern der Leitungsbestand zu erheben. Eine etwaige Verlegung bestehender, unterirdischer Leitungen geht zu Lasten des Veranlassers.

3.3 Archäologische Denkmalpflege
Sollten bei Erdarbeiten Funde (beispielsweise Scherben, Metallteile, Knochen) und Befunde (z. B. Mauern, Gräber, Gruben, Brandschichten) entdeckt werden, ist das Landesamt für Denkmalpflege beim Regierungspräsidium Stuttgart (Abt. 8) unverzüglich zu benachrichtigen. Fund und Fundstelle sind bis zur sachgerechten Begutachtung, mindestens bis zum Ablauf des 4. Werktags nach Anzeige, unverändert im Boden zu belassen. Die Möglichkeit zur fachgerechten Dokumentation und Fundbergung ist einzuräumen.
Auf § 20 DSchG (Denkmalschutzgesetz) wird verwiesen.

Nördlich des Plangebietes liegt ein ausgedehntes vorgeschichtliches Grabhügelfeld. Nach Ausweis von Luftbildern und Geländescans sind die einzelnen Hügel hier noch recht gut erhalten. Mit Flachgräbern und archäologischen Niederschlägen von zugehörigen Siedlungen sowie einem Ausgreifen dieses Kulturdenkmals gem. § 2 DSchG in das Plangebiet ist deshalb zu rechnen.
An der Erhaltung ausgewiesener archäologischer Kulturdenkmale besteht grundsätzlich ein öffentliches Interesse.

Um eine undokumentierte Zerstörung zu verhindern bitten wir folgendes zu beachten:
1. Der vorgesehene Beginn von Erschließungsmaßnahmen oder sonstigen Erdarbeiten ist der Archäologischen Denkmalpflege wenigstens 3 Wochen vor geplantem Termin anzuzeigen.
2. Die Erdarbeiten erfolgen im Beisein eines Mitarbeiters der Archäologischen Denkmalpflege, der den Oberbodenabtrag begleitet.
3. Gegebenenfalls ist ausreichend Zeit zur Fundbergung und Dokumentation einzuräumen.

Vorsorglich weisen wir darauf hin, dass im Falle notwendiger Rettungsgrabungen durch das LAD die Bergung und Dokumentation der Kulturdenkmale mehrere Wochen /ggf. Monate in Anspruch nehmen kann und durch den Vorhabenträger finanziert werden muss.

3.4 Wasser- und Bodenschutz
Bei allen Bau- und Planungsmaßnahmen sind die Grundsätze des schonenden und sparsamen Umgangs mit Boden (§ 4 BodSchG, §§ 1, 202 BauGB, §§ 1, 2 NatSchG) zu berücksichtigen. Die Bodenschutzbehörden sind zu beteiligen (§§ 5, 6 BodSchG).
Der im Zuge der Baumaßnahmen anfallende Erdaushub ist möglichst im Plangebiet zu verwerten. Bodenversiegelungen sind auf das notwendige Mindestmaß zu beschränken.

Das Plangebiet liegt in der Zone IIIB des mit Rechtsverordnung vom Landratsamt Biberach am 23.01.2004 festgesetzten Wasserschutzgebiet „Gesamt Illertal“. Die Rechtsverordnung ist zu beachten. Auf die Verbotstatbestände dieser Rechtsverordnung wird hingewiesen.

3.5 Hinweise zu Photovoltaik- und Solarthermie-Kollektoren
Die Anlagenelemente müssen dem neuesten Stand des Insektenschutzes bei PV-Anlagen entsprechen.

3.6 Niederschlagswasser
Auf Flächen deren Niederschlagswasser über die Regenwasserkanalisation geleitet wird, darf kein Abwasser im Sinne von verunreinigtem Wasser anfallen. Entsprechende Arbeiten wie z. B. Autowäsche, Reinigungsarbeiten, sind nicht zulässig. Drainagen sind nur zulässig, wenn kein Grundwasser abgesenkt wird und der Ablauf der Drainage in die Regenwasserkanalisation erfolgt. Andere Drainagen sind nicht zulässig. Sickerschächte sind unzulässig. Werden Regenwasserzisternen für den Betriebswasserbedarf installiert, sind diese dem Gesundheitsamt schriftlich zu melden.

3.7 Immissionen
An das Plangebiet grenzen im Westen, Norden und Osten landwirtschaftlich genutzte Grundstücke. Es wird auf die zu erduldenden, nutzungsbedingten Störeinflüsse hingewiesen, wie z.B. unverzichtbare Düngearbeiten oder Lärm durch landwirtschaftliche Maschinen.
Nordöstlich des Plangebietes in ca. 750 m Entfernung befindet sich ein Verkehrslandeplatz. Es wird auf möglichen Fluglärm hingewiesen.

3.8 Landesstraßen L260 / L300

Anbauverbotsstreifen
Die zwischen den Baugrenzen und den Straßenflächen bestehenden Grundstücksflächen gelten als nicht überbaubare Grundstücksstreifen. Auf diesen nicht überbaubaren Flächen dürfen Nebenanlagen i. S. von § 14 Baunutzungsverordnung (BauNVO), d. h. Hochbauten, Stellplätze und Garagen und sonstige Nebenanlagen, z. B. Lagerflächen usw. nicht zugelassen werden(§ 12 Abs. 6 und§ 14 Abs. 1 BauNVO). Nebenanlagen, welche nach § 14 BauNVO in einem Baugebiet auch außerhalb der Baugrenzen zulässig sein können, dürfen innerhalb des vorgenannten Anbauverbots nicht ohne die ausdrückliche Zustimmung des Straßenamtes zugelassen werden.

Nach der LBO genehmigungsfreie Anlagen bedürfen in diesem Bereich der Genehmigung des Straßenamtes. Werbeanlagen wegen der Beeinträchtigung des Schutzzweckes des § 16 LBO nicht zugelassen werden können. Im Anbauverbotsstreifen sind Werbeanlagen wegen der Beeinträchtigung des Schutzzweckes des § 16 LBO nicht zugelassen.

Straßenbegleitgrün
Von der Bepflanzung dürfen keine unmittelbaren Gefahren für den Verkehr ausgehen. Der gemäß RPS 2009 einzuhaltende Mindestabstand für Bäume vom Rand der befestigten Fahrbahn beträgt 7,50 m. Bei Unterschreitung des Mindestabstandes sind passive Schutzeinrichtungen erforderlich.
Es wird vorsorglich darauf hingewiesen, dass sich die Straßenbauverwaltung deshalb an den Kosten notwendig werdender erforderlichen Schutzeinrichtungen nicht beteiligen kann.

Immissionen
Das Baugebiet wird im Immissionsbereich der überörtlichen Straße, besonders im Schalleinwirkungsbereich, liegen. Es ist durch die überörtliche Straße vorbelastet. Der Straßenbaulastträger ist deshalb nicht verpflichtet, sich an den Kosten evtl. notwendig werdender Schutzmaßnahmen (z. B. Schallschutz) zu beteiligen.
Für die Planung schutzbedürftiger Nutzungen im Schalleinwirkungsbereich dieser Straße sind zur Vermeidung von Lärmproblematiken die schalltechnischen Orientierungswerte für Verkehrslärm nach DIN 18005 Beiblatt 1 (Werte in dB (A) einzuhalten werden.

Reflexionen durch Photovoltaikanlagen
Die künftigen Bauherren werden darauf aufmerksam gemacht, dass bei der Errichtung von Photovoltaikanlagen auf den Dächern der geplanten Gebäude keine Reflexionen z. B. durch Spiegelung der Sonnenstrahlen in den Modulen auftreten dürfen, die die Verkehrsteilnehmer auf der klassifizierten Straße erreichen. Die Elemente sind deshalb in einem Winkel anzuordnen, der eine Reflexion bis auf eine Ebene von 3 m über der Fahrbahn ausschließt. Alternativ kann die Reflexionswirkung auch durch eine entsprechende Bauart ausgeschlossen werden.

Entwässerung
Der Landesstraße 260 und L 300 sowie ihren jeweiligen Entwässerungseinrichtungen darf vom gesamten Geltungsbereich des Bebauungsplanes einschließlich der Erschließungsstraßen kein Oberflächenwasser zugeführt werden.

Ver- und Entsorgungsleitungen
Anpassungsarbeiten, Verlegen von Ver- und Entsorgungsleitungen oder sonstige Veränderungen im Bereich des Straßenkörpers der klassifizierten Straßen dürfen nur mit besonderer Erlaubnis und nach den näheren Angaben der Straßenbauverwaltung bzw. nur auf gesonderten Antrag nach Abschluss einer entsprechenden vertraglichen Regelung mit dem Landratsamt Biberach vorgenommen werden.

3.9 Wärmepumpen
Durch den Betrieb von Luft-Wasser-Wärmepumpen kann es bei ungünstiger Aufstellung durch tonhaltige Geräusche zu Lärmbelästigungen in der Nachbarschaft kommen. Es wird deshalb empfohlen solche Geräte abgewandt von Wohn-, Schlaf- und Terrassenbereichen benachbarter Wohngebäude zu errichten bzw. zusätzliche Schalldämmmaßnahmen durchzuführen. Auf jeden Fall sollte an den benachbarten Baugrenzen oder Wohngebäuden der Beurteilungspegel nach der TA Lärm von 34 dB(A) nicht überschritten werden.

3.10 Vorhandener Regenwasserkanal / verdolter Bachlauf
Im Bereich des verdolten Bachlaufes kann mit austretendem Wasser gerechnet werden. Es wird empfohlen, die Kellergeschosse in diesem Bereich wasserdicht mit einer „weißen Wanne“ zu errichten.

3.11 Verkehrslandeplatz
Nordöstlich des Plangebietes in ca. 750 m Entfernung befindet sich ein Verkehrslandeplatz. Der Flugplatz ist für das geplante Wohngebiet nicht immissionsrelevant, da nachts kein Flugbetrieb stattfindet.

3.12 Höhensystem
Die im Plan eingetragenen Höhen beziehen sich auf das "Deutsche Haupthöhennetz 1912“, abgekürzt „DHHN 12" (Angaben in m über Normal Null).

3.13 Geotechnik
Das Plangebiet befindet sich auf Grundlage der am LGRB vorhandenen Geodaten im Verbreitungsbereich von Sedimenten der Rheingletscher-Niederterrassenschotter.
In Anbetracht der Größe des Plangebiets geht das LGRB davon aus, dass eine ingenieurgeologische Übersichtsbegutachtung durch ein privates Ingenieurbüro durchgeführt wurde/wird. Darin sollten die generellen Baugrundverhältnisse untersucht sowie allgemeine Empfehlungen zur Erschließung und Bebauung abgegeben werden. Ferner sollten darin die Notwendigkeit und der Umfang objektbezogener Baugrundgutachten gemäß DIN EN 1997-2 bzw. DIN 4020 beschrieben werden.

Allgemeine Hinweise:
Die lokalen geologischen Untergrundverhältnisse können dem bestehenden Geologischen Kartenwerk, eine Übersicht über die am LGRB vorhandenen Bohrdaten der Homepage des LGRB (http://www.lgrb-bw.de) entnommen werden. Des Weiteren verweisen wir auf unser Geotop-Kataster, welches im Internet unter der Adresse http://lgrb-bw.de/geotourismus/geotope (Anwendung LGRB-Mapserver Geotop-Kataster) abgerufen werden kann.

## 4. Anlagen zum Bebauungsplan

4.1 Begründung in der Fassung vom 02.03.2020

# TEIL II : ÖRTLICHE BAUVORSCHRIFTEN

## Rechtsgrundlagen

| | |
|---|---|
| Landesbauordnung für Baden-Württemberg (LBO) | i. d. F. vom 05. März 2010 (GBl. S. 358), zuletzt geändert durch Gesetz vom 18. Juli 2019 (Gbl. S. 313) |
| Gemeindeordnung (GemO) für Baden-Württemberg | i. d. F. vom 24.07.2000 (GBl. S. 581), zuletzt geändert durch Artikel 16 des Gesetzes vom 21. Mai 2019 (GBl. S. 161, 186) |

Es wird Folgendes festgesetzt:

## Räumlicher Geltungsbereich

Der räumliche Geltungsbereich der örtlichen Bauvorschriften ist im Lageplan schwarz gestrichelt umrandet.

## 1. Örtliche Bauvorschriften (Gestaltungsvorschriften gem. § 74 LBO)

1.1 Äußere Gestaltung baulicher Anlagen — § 74 (1) 1 LBO
Nicht zulässig zur Fassadengestaltung sind folgende Materialien:
Verspiegelte Glasflächen. Solar- und Photovoltaikanlagen sind hiervon ausgenommen.

1.2 Dachform und Dachgestaltung — § 74 (1) 1 LBO
Zulässig sind geneigte Dächer mit einer Dachneigung von 18° - 40°.
Bei Doppelhäusern ist bei beiden Haushälften dieselbe Dachneigung zu errichten.
Bei Garagen sind geringere Dachneigungen bis minimal 10° sowie Flachdächer zulässig.
Bei Carports sind ebenfalls Flachdächer zulässig.

Füllschema der Nutzungsschablone

| Örtliche Bauvorschriften |
|---|
| Dachform / Dachneigung |

1.3 Dacheindeckung — § 74 (1) 1 LBO
Die Dachflächen der Hauptgebäude bei geneigten Dächern sind mit Dachziegeln, Dachsteinen oder beschichteten Metallelementen in brauner, rotbrauner, grauer oder anthrazit Farbe einzudecken. Für Dachgauben ist eine andere Eindeckung zulässig.
Zur Dacheindeckung nicht zulässig sind unbeschichtete Metalle und Materialien, die wassergefährdende Stoffe enthalten und in ihrer Art und Menge geeignet sind, über die zu versickernden Niederschläge das Grundwasser und den Boden zu verunreinigen.

1.4 Dachaufbauten — § 74 (1) 1 LBO
Ab 30° geneigten Dächern sind Dachaufbauten (z.B. Gaupen, Quergiebel und Nebenfirste) zulässig. Pro Dachseite ist nur eine Form von Dachaufbauten zulässig. Widerkehren bleiben davon unberührt.

1.5 Gestaltung der unbebauten Grundstücksflächen — § 74 (1) 3 LBO
Innerhalb der Baugrundstücke sollten für Zugänge, Zufahrten und offene Stellplätze nach Möglichkeit nur wasserdurchlässige Beläge (z.B. Rasengittersteine, wasserdurchlässiges Betonpflaster, Schotterrasen oder Pflaster mit breiten Fugen) verwendet werden.
Sonstige unbefestigte Grundstücksflächen sind als Grünflächen und / oder Hausgärten anzulegen und mit standortgerechten Gehölzen und Stauden zu bepflanzen.
Im Vorgartenbereich sind Stein-, Schotter- oder Kiesgärten nicht zulässig.

1.6 Einfriedungen an öffentlichen Verkehrsflächen — § 74 (1) 3 LBO
Einfriedungen müssen zur öffentlichen Verkehrsfläche einen Mindestabstand von 0,20 m einhalten. Entlang der öffentlichen Verkehrsflächen darf die Höhe der Einfriedungen 0,8 m nicht überschreiten. Zulässig im Bereich der öffentlichen Verkehrsflächen sind:
- Holzzäune
- freiwachsende landschaftsgebundene Hecken,
- Metallzäune, die locker / abwechselnd mit Kletterpflanzen und einzelnen Sträuchern zu bepflanzen sind,
- Mauern und Gabionenwände

Generell nicht zulässig sind Stacheldrahtzäune.

1.7 Werbeanlagen — § 74 (1) 2 LBO
Werbeanlagen sind grundsätzlich nur innerhalb der überbaubaren Grundstücksflächen zulässig. Werbeanlagen sind auf Dachflächen nicht zulässig. Es sind nur unbeleuchtete Werbeanlagen zulässig.

1.8 Stellplatznachweis — § 74 (2) 2 LBO
Die Zahl der herzustellenden notwendigen Stellplätze beträgt 2 Stellplätze pro Wohneinheit.

Ausnahmen sind bei Wohnungen für Seniorenwohnanlagen / Senioren gerechtes Wohnen zulässig.

## 2. Anlagen zu den örtlichen Bauvorschriften

2.1 Begründung der örtlichen Bauvorschriften in der Fassung vom 02.03.2020

## VERFAHRENSVERMERKE

| | | |
|---|---|---|
| 1. Aufstellungsbeschlüsse durch den Gemeinderat gem. § 2 (1) BauGB | am | 07.05.2018 |
| 2. Bekanntmachung der Aufstellungsbeschlüsse gem. § 2(1) BauGB | am | 17.05.2018 |
| 3. Bekanntmachung der frühzeitigen Beteiligung der Öffentlichkeit gem. § 3 (1) BauGB | am | 17.05.2018 |
| 4. Frühzeitige Beteiligung der Öffentlichkeit und Behörden gem. § 3 (1) und § 4 (1) BauGB | vom<br>bis | 25.05.2018<br>29.06.2018 |
| 5. Abwägung der eingegangenen Stellungnahmen gem. § 4 (1) BauGB / Billigung des Bebauungsplanentwurfes und der örtlichen Bauvorschriften und Auslegungsbeschlüsse durch den Gemeinderat | am | 09.12.2019 |
| 6. Bekanntmachung der öffentlichen Auslegungen gem. § 3 (2) und § 4 (2) BauGB | am | 12.12.2019 |
| 7. Öffentliche Auslegung des Bebauungsplanentwurfes und der örtlichen Bauvorschriften mit Begründungen i.d. Fassung vom 18.11.2019 gem. § 3 (2) und § 4 (2) BauGB | vom<br>bis | 23.12.2019<br>31.01.2020 |
| 8. Abwägung der eingegangenen Stellungnahmen gem. § 4 (2) BauGB und Satzungsbeschlüsse durch den Gemeinderat gem. § 10 BauGB und § 74 (7) LBO | am | 16.03.2020 |

Tannheim, den 20.03.2020

gez. Thomas Wonhas
(BÜRGERMEISTER)

## AUSFERTIGUNG

Der textliche und zeichnerische Inhalt dieses Bebauungsplanes und der örtlichen Bauvorschriften mit Begründungen stimmen mit den Satzungsbeschlüssen vom 16.03.2020 überein.
Die Verfahren wurden ordnungsgemäß durchgeführt.

Tannheim, den 20.03.2020

gez. Thomas Wonhas
(BÜRGERMEISTER)

Ortsübliche Bekanntmachung und Beginn der Rechtsverbindlichkeit des Bebauungsplanes und der örtlichen Bauvorschriften mit Begründungen am 26.03.2020

Tannheim, den 26.03.2020

gez. Thomas Wonhas
(BÜRGERMEISTER)

GEMEINDE TANNHEIM

LAGEPLANBEZEICHNUNG:
BEBAUUNGSPLAN UND ÖRTLICHE BAUVORSCHRIFTEN
"BERKHEIMER WEG"

M. 1:500

PLANVERFASSER:
**PLANWERKSTATT a.B.**
**Rainer Waßmann** Stadtplanung
Bodanstraße 38
88079 Kressbronn
Tel. (075 43) 962 98 13
Fax (075 43) 962 98 20

AUFTRAGGEBER
Gemeinde Tannheim
Rathausplatz 1
88459 Tannheim
Telefon: (08395) 922 - 0
Fax: (08395) 7618

DATUM: 02.03.2020

PLANVERFASSER:
gez. Rainer Waßmann

AUFTRAGGEBER
gez. Thomas Wonhas, Bürgermeister

REG.-NR.:

Fertigung